국립금오공과대학교
Kumoh National Institute of Technology

디지털관 시청각실 및 대강의실 외 기타 노후 냉난방기 교체 전기공사

2025. 12. .

사무국 시설안전과
전화 : 054)478-7143
팩스 : 054)478-7156

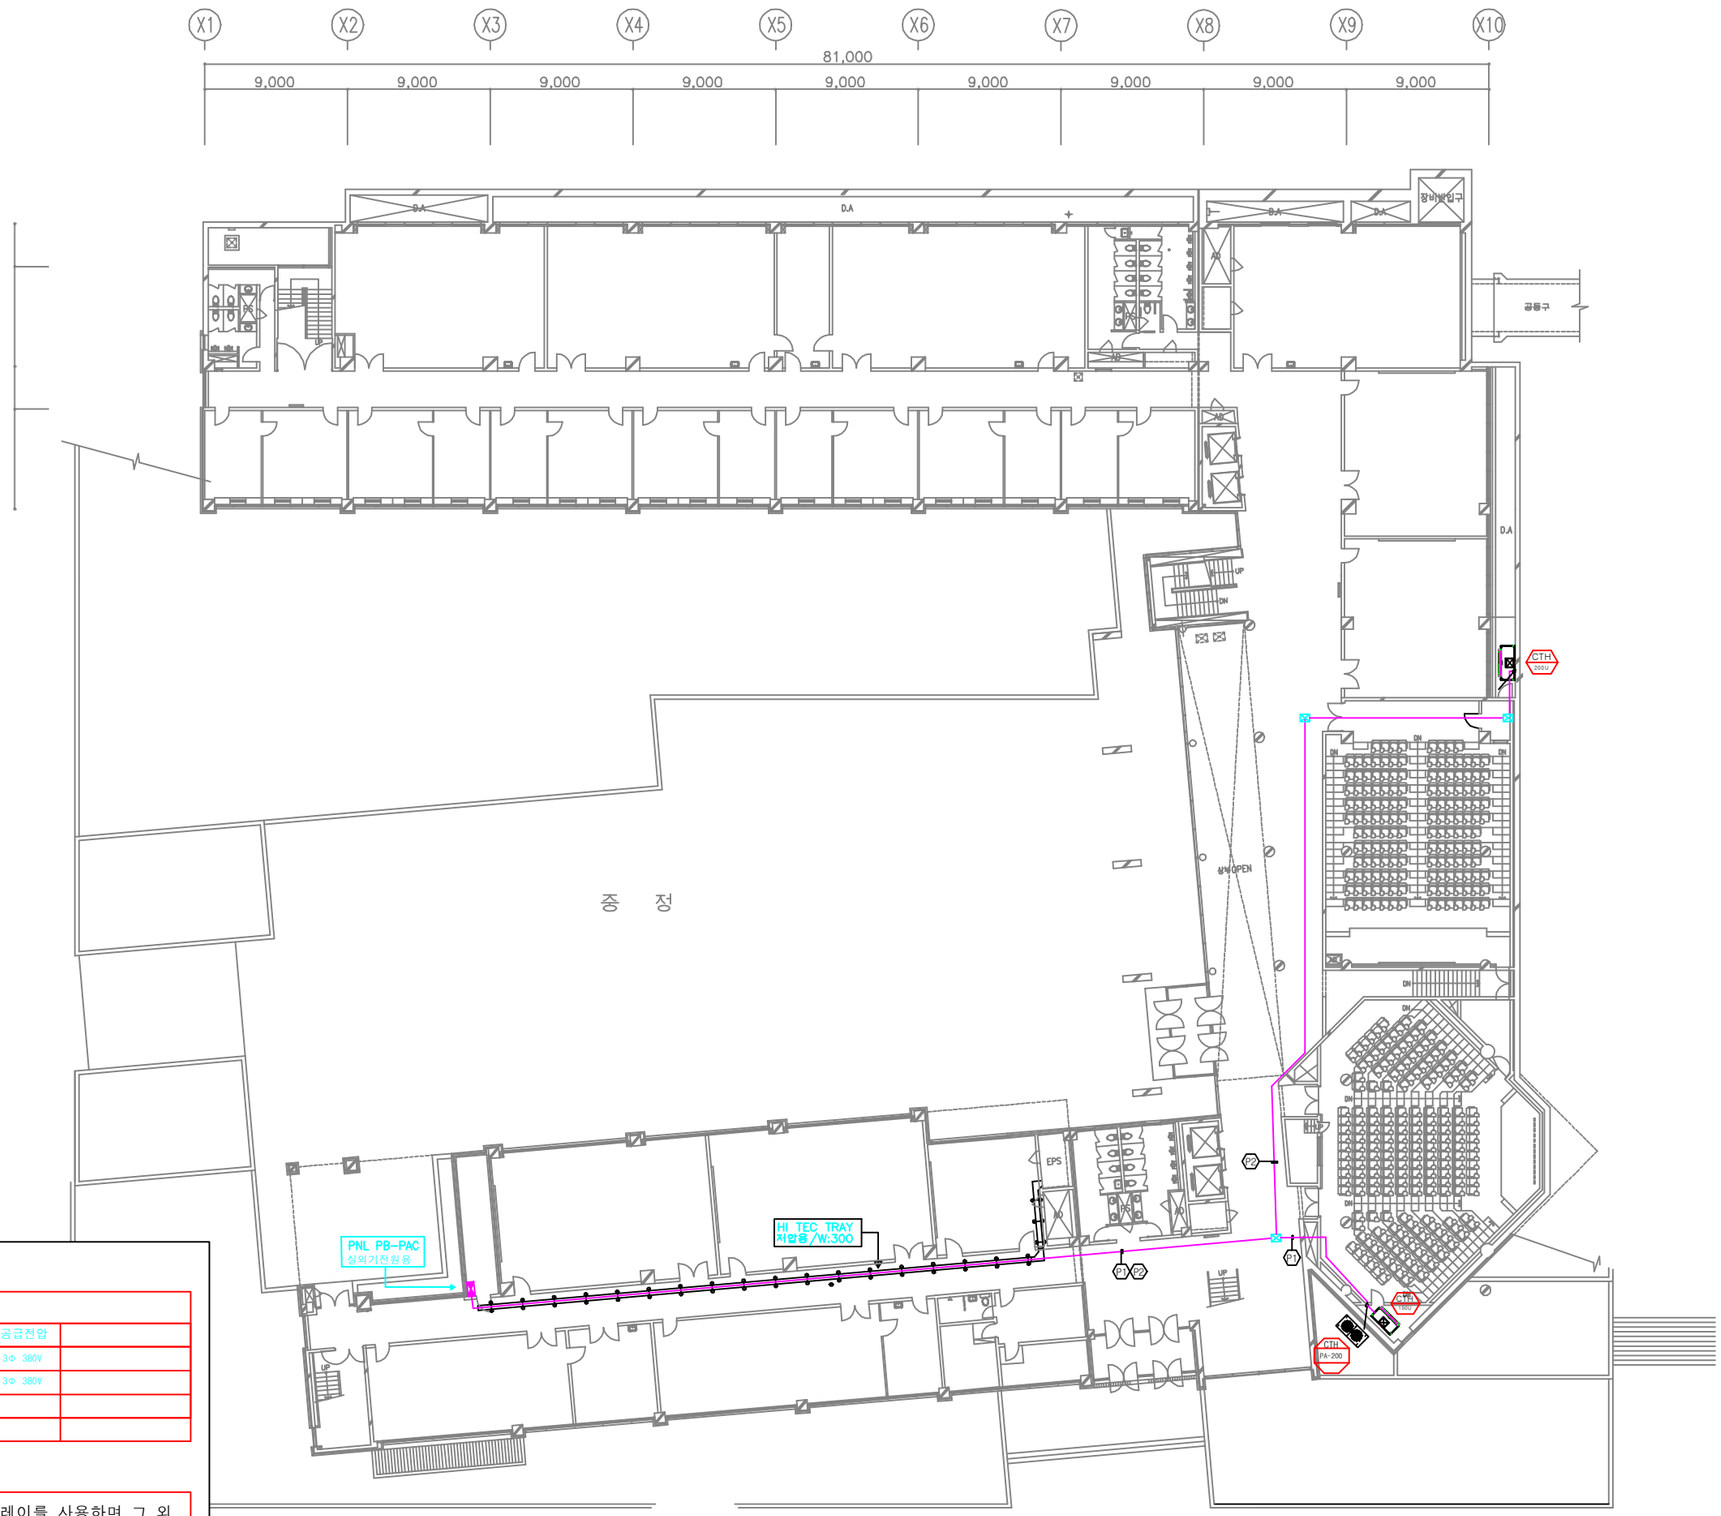

CABLE SCHEDULE

기기 및 케이블 목록

번호	CABLE SCHEDULE	공급전압	
P1	F-CV 4C/35㎟, 강제전선관(54c)	3Φ 380V	
P2	F-CV 1C/50㎟ × 3L, GV 25㎟ 강제전선관(54C)	3Φ 380V	

N O T E

1. 항온항습기 메인 전원은 트레이구간은 트레이를 사용하며 그 외 구간은 강제전선관을 사용한다.
2. 실외기 전원 배관 배선은 항온항습기 설치 업체에서 시공한다
3. 반드시 시공전 감독과 협의 후 시공한다.

국립금오공과대학교
Kumoh National Institute of Technology

kit

PROJECT TITLE

디지털관 시청각실 및 대강의실 외 기타 노후 냉난방기 교체 전기공사

DRAWING TITLE

디지털관 지하 1층 배선 평면도

SCALE

A3 = 1 / 1

DATE

2025. 12.

CHECKED BY

주무관 권 순 재

APPROVED BY

팀 장 이 인 호

REMARK

DRAWING NO.

D-01